


LAGEPLAN

- ZEICHNERISCHER TEIL -
zum Bauvertrag (2 BauVorlVd)

WA	II-IV
04	(12)+Gau
b	FD

Auf Deckblatt geändert:
Rommelshausen den 11.11.19

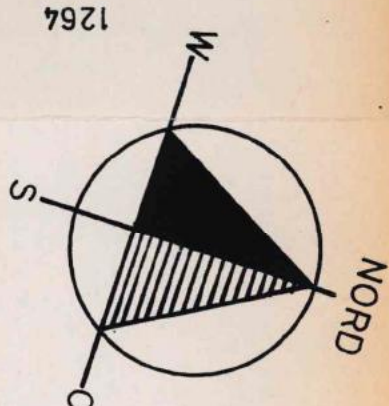

Stettiner Straße

WA	I+D
035	(07)
SD 65°	

Kniestock max. 0,5m

Ebniseeweg


FUSSWEG

FUSSWEG

Königsberger Straße

ASSTAB 1:500

Unterirdische Versorgungsleitungen u. dgl.
sind dem Planfertiger nicht bekannt und im
vorliegenden Plan nicht enthalten.

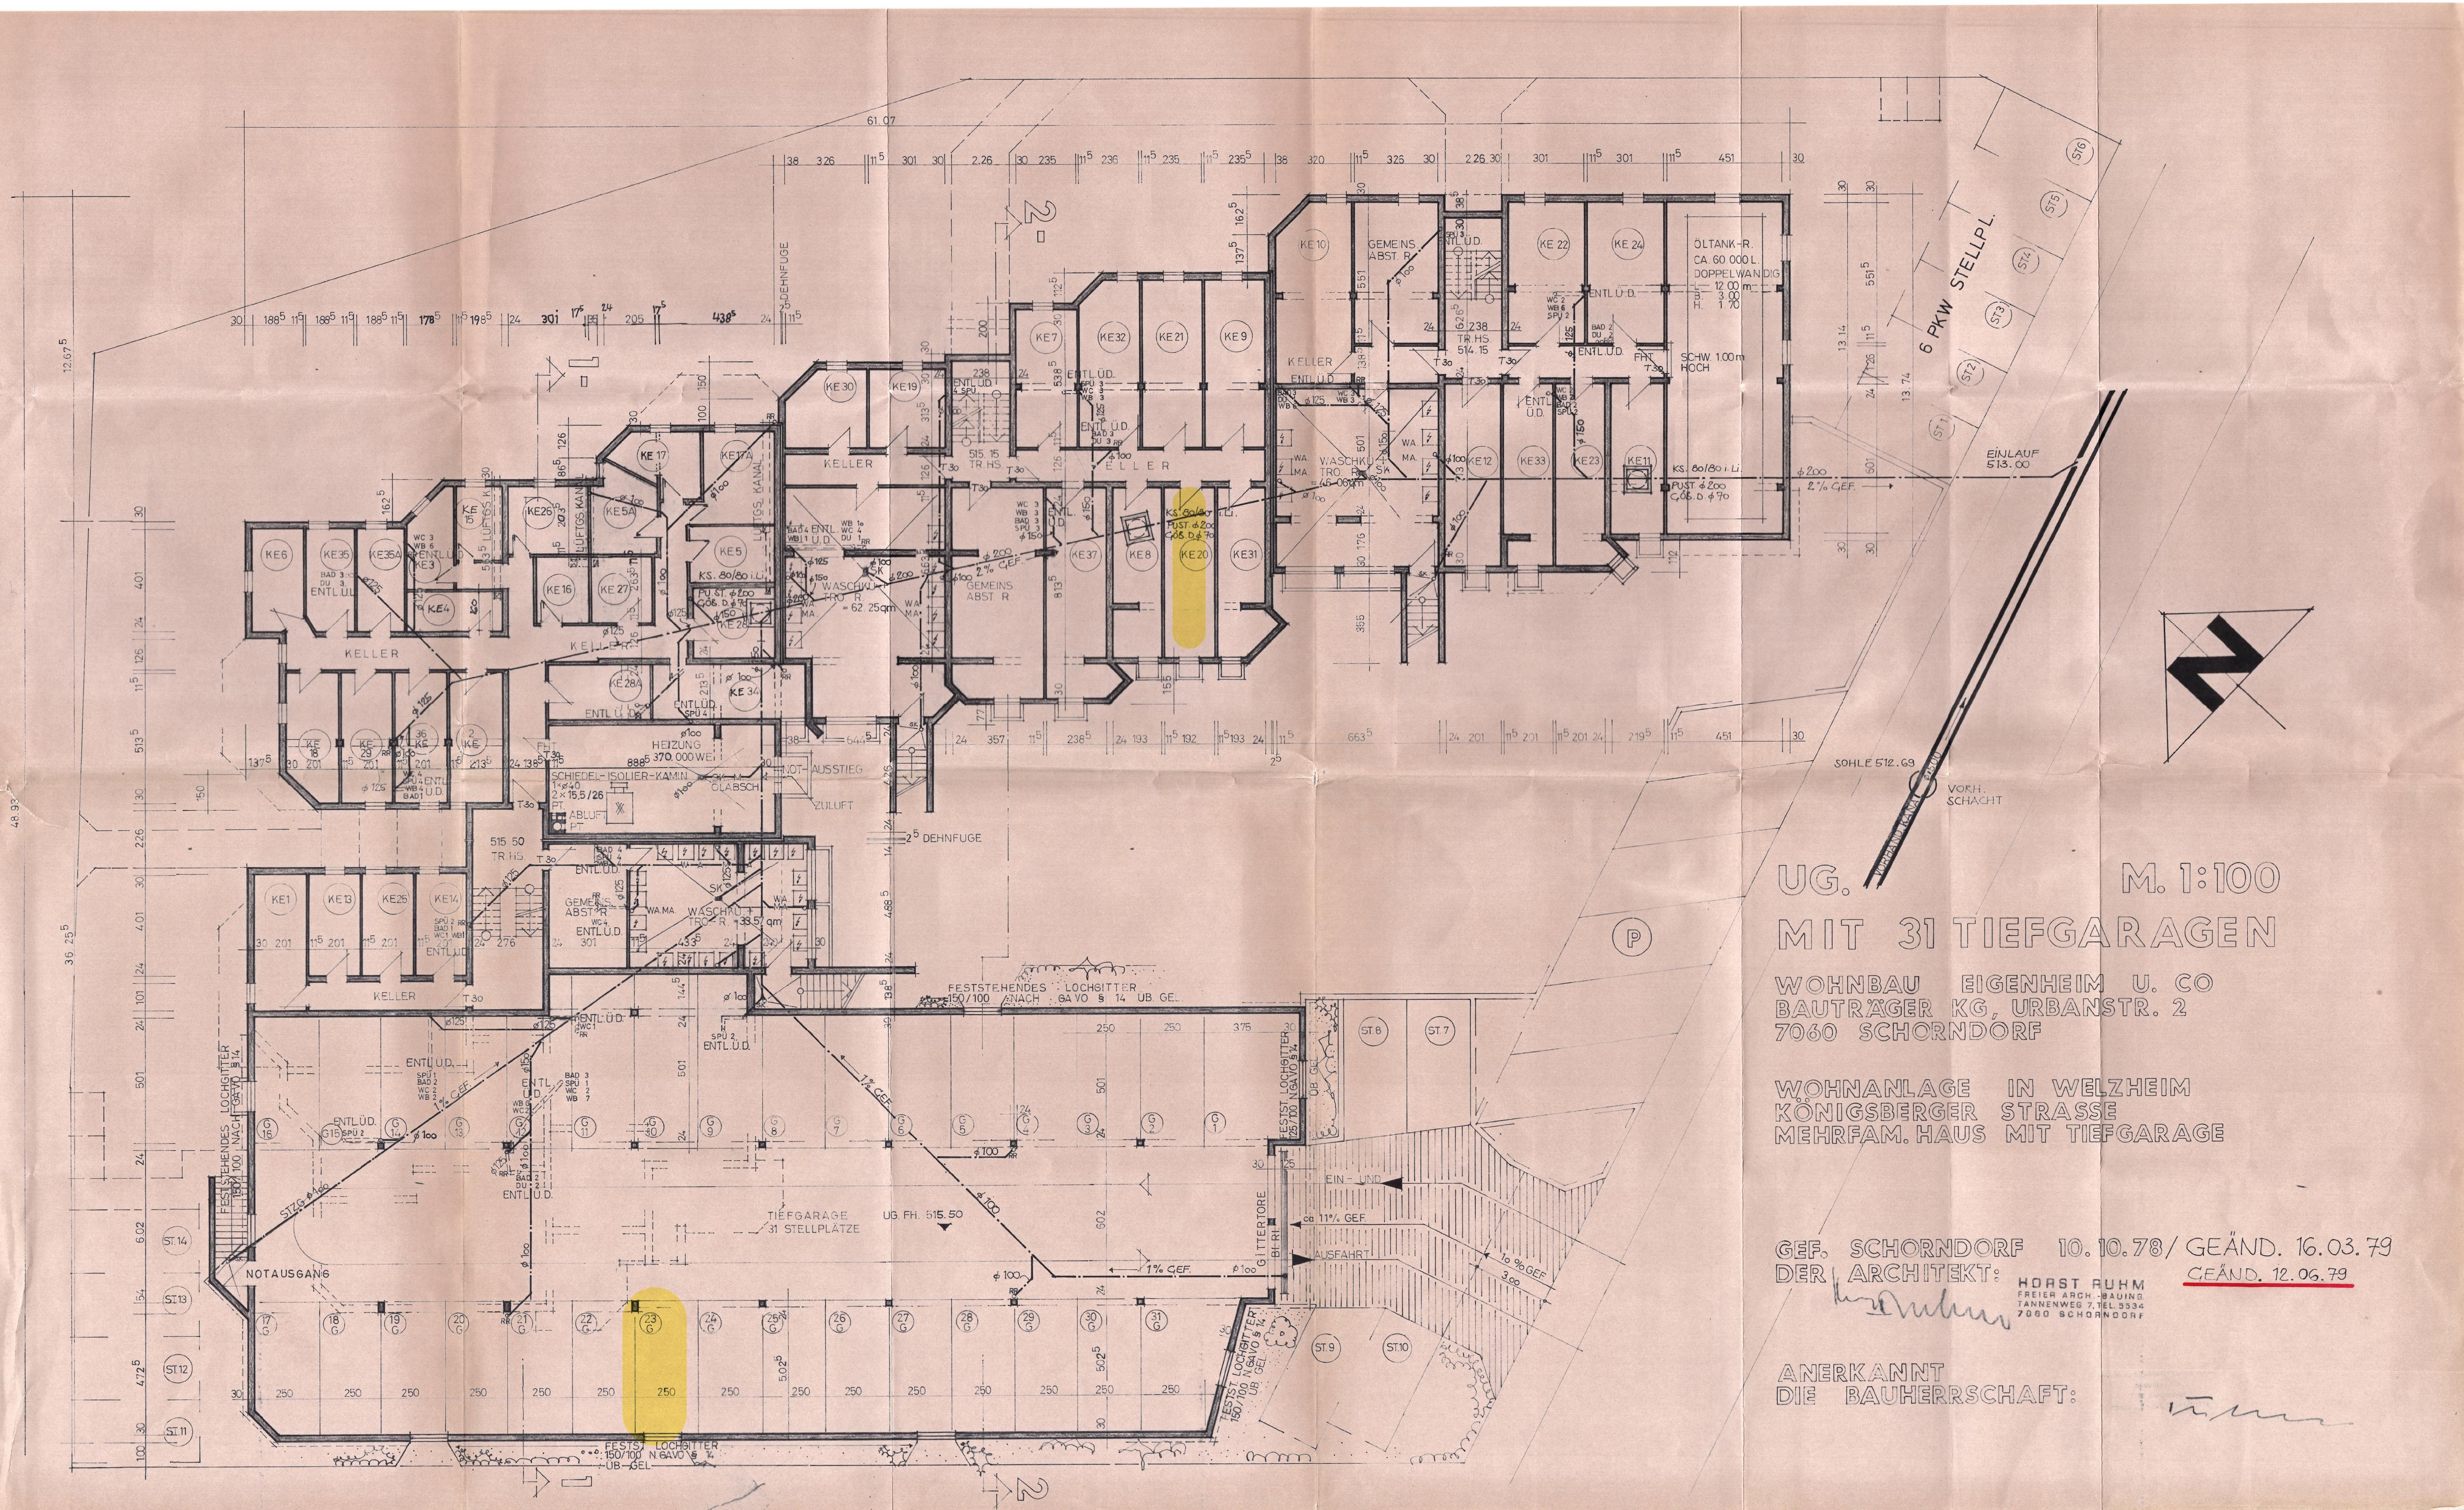

UG. M. 1:100
MIT 31 TIEFGARAGEN


WOHNBAU EIGENHEIM U. CO
BAUTRÄGER KG, URBANSTR. 2
7060 SCHORNDORF

WOHNANLAGE IN WELZHEIM
KÖNIGSBERGER STRASSE
MEHRFAM. HAUS MIT TIEFGARAGE

GEF. SCHORNDORF 10.10.78/GEÄND. 16.03.79
DER ARCHITEKT: CEÄND. 12.06.79

HORST RUHM
FREIER ARCH.-BAUING
TANNENWEG 7, TEL. 5534
7060 SCHORNDORF

ANERKANNT
DIE BAUHERRSCHAFT:

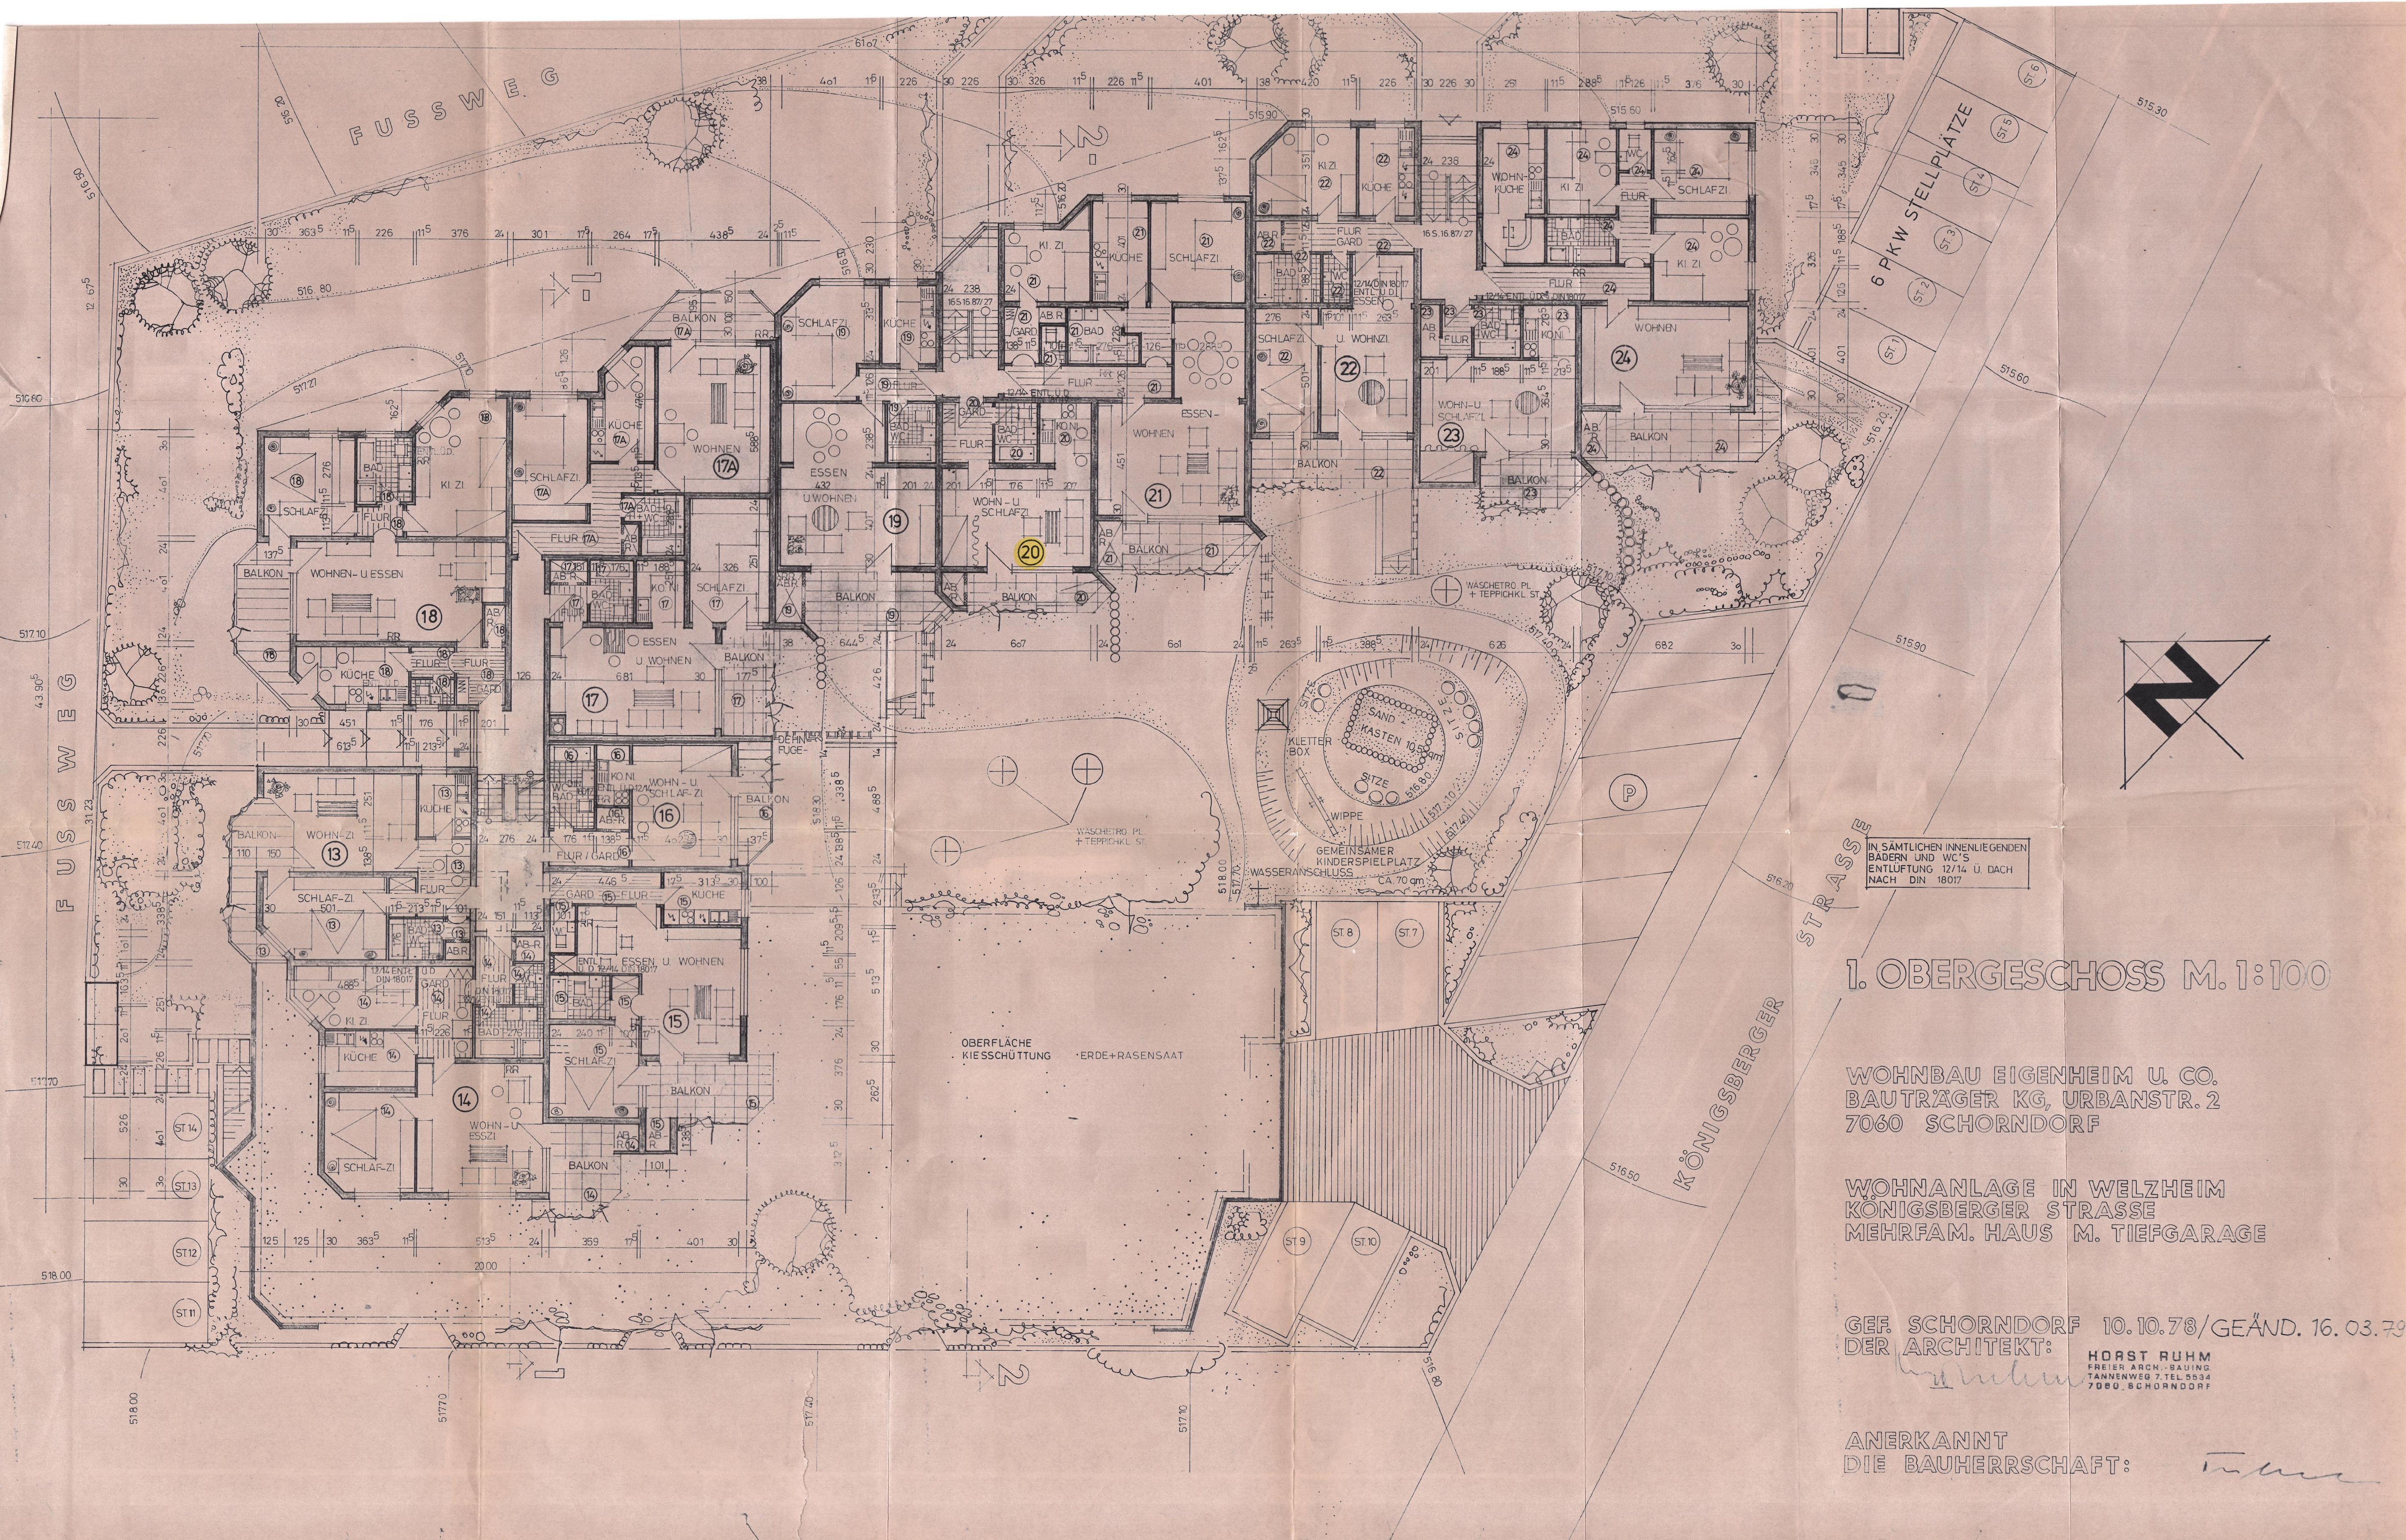

IN SÄMTLICHEN INNENLIEGENDEN
BÄDERN UND WC'S
ENTLÜFTUNG 12/14 U. DACH
NACH DIN 18017

1. OBERGESCHOSS M. 1:100

WOHNBAU EIGENHEIM U. CO.
BAUTRÄGER KG, URBANSTR. 2
7060 SCHORNDORF

WOHNANLAGE IN WELZHEIM
KÖNIGSBERGER STRASSE
MEHRFAM. HAUS M. TIEFGARAGE

GEF. SCHORNDORF 10.10.78/GEÄND. 16.03.79
DER ARCHITEKT:

HORST RUHM
FREIER ARCH.-BAUING
TANNENWEG 7, TEL. 5534
7080 SCHORNDORF

ANERKANNT
DIE BAUHERRSCHAFT: